

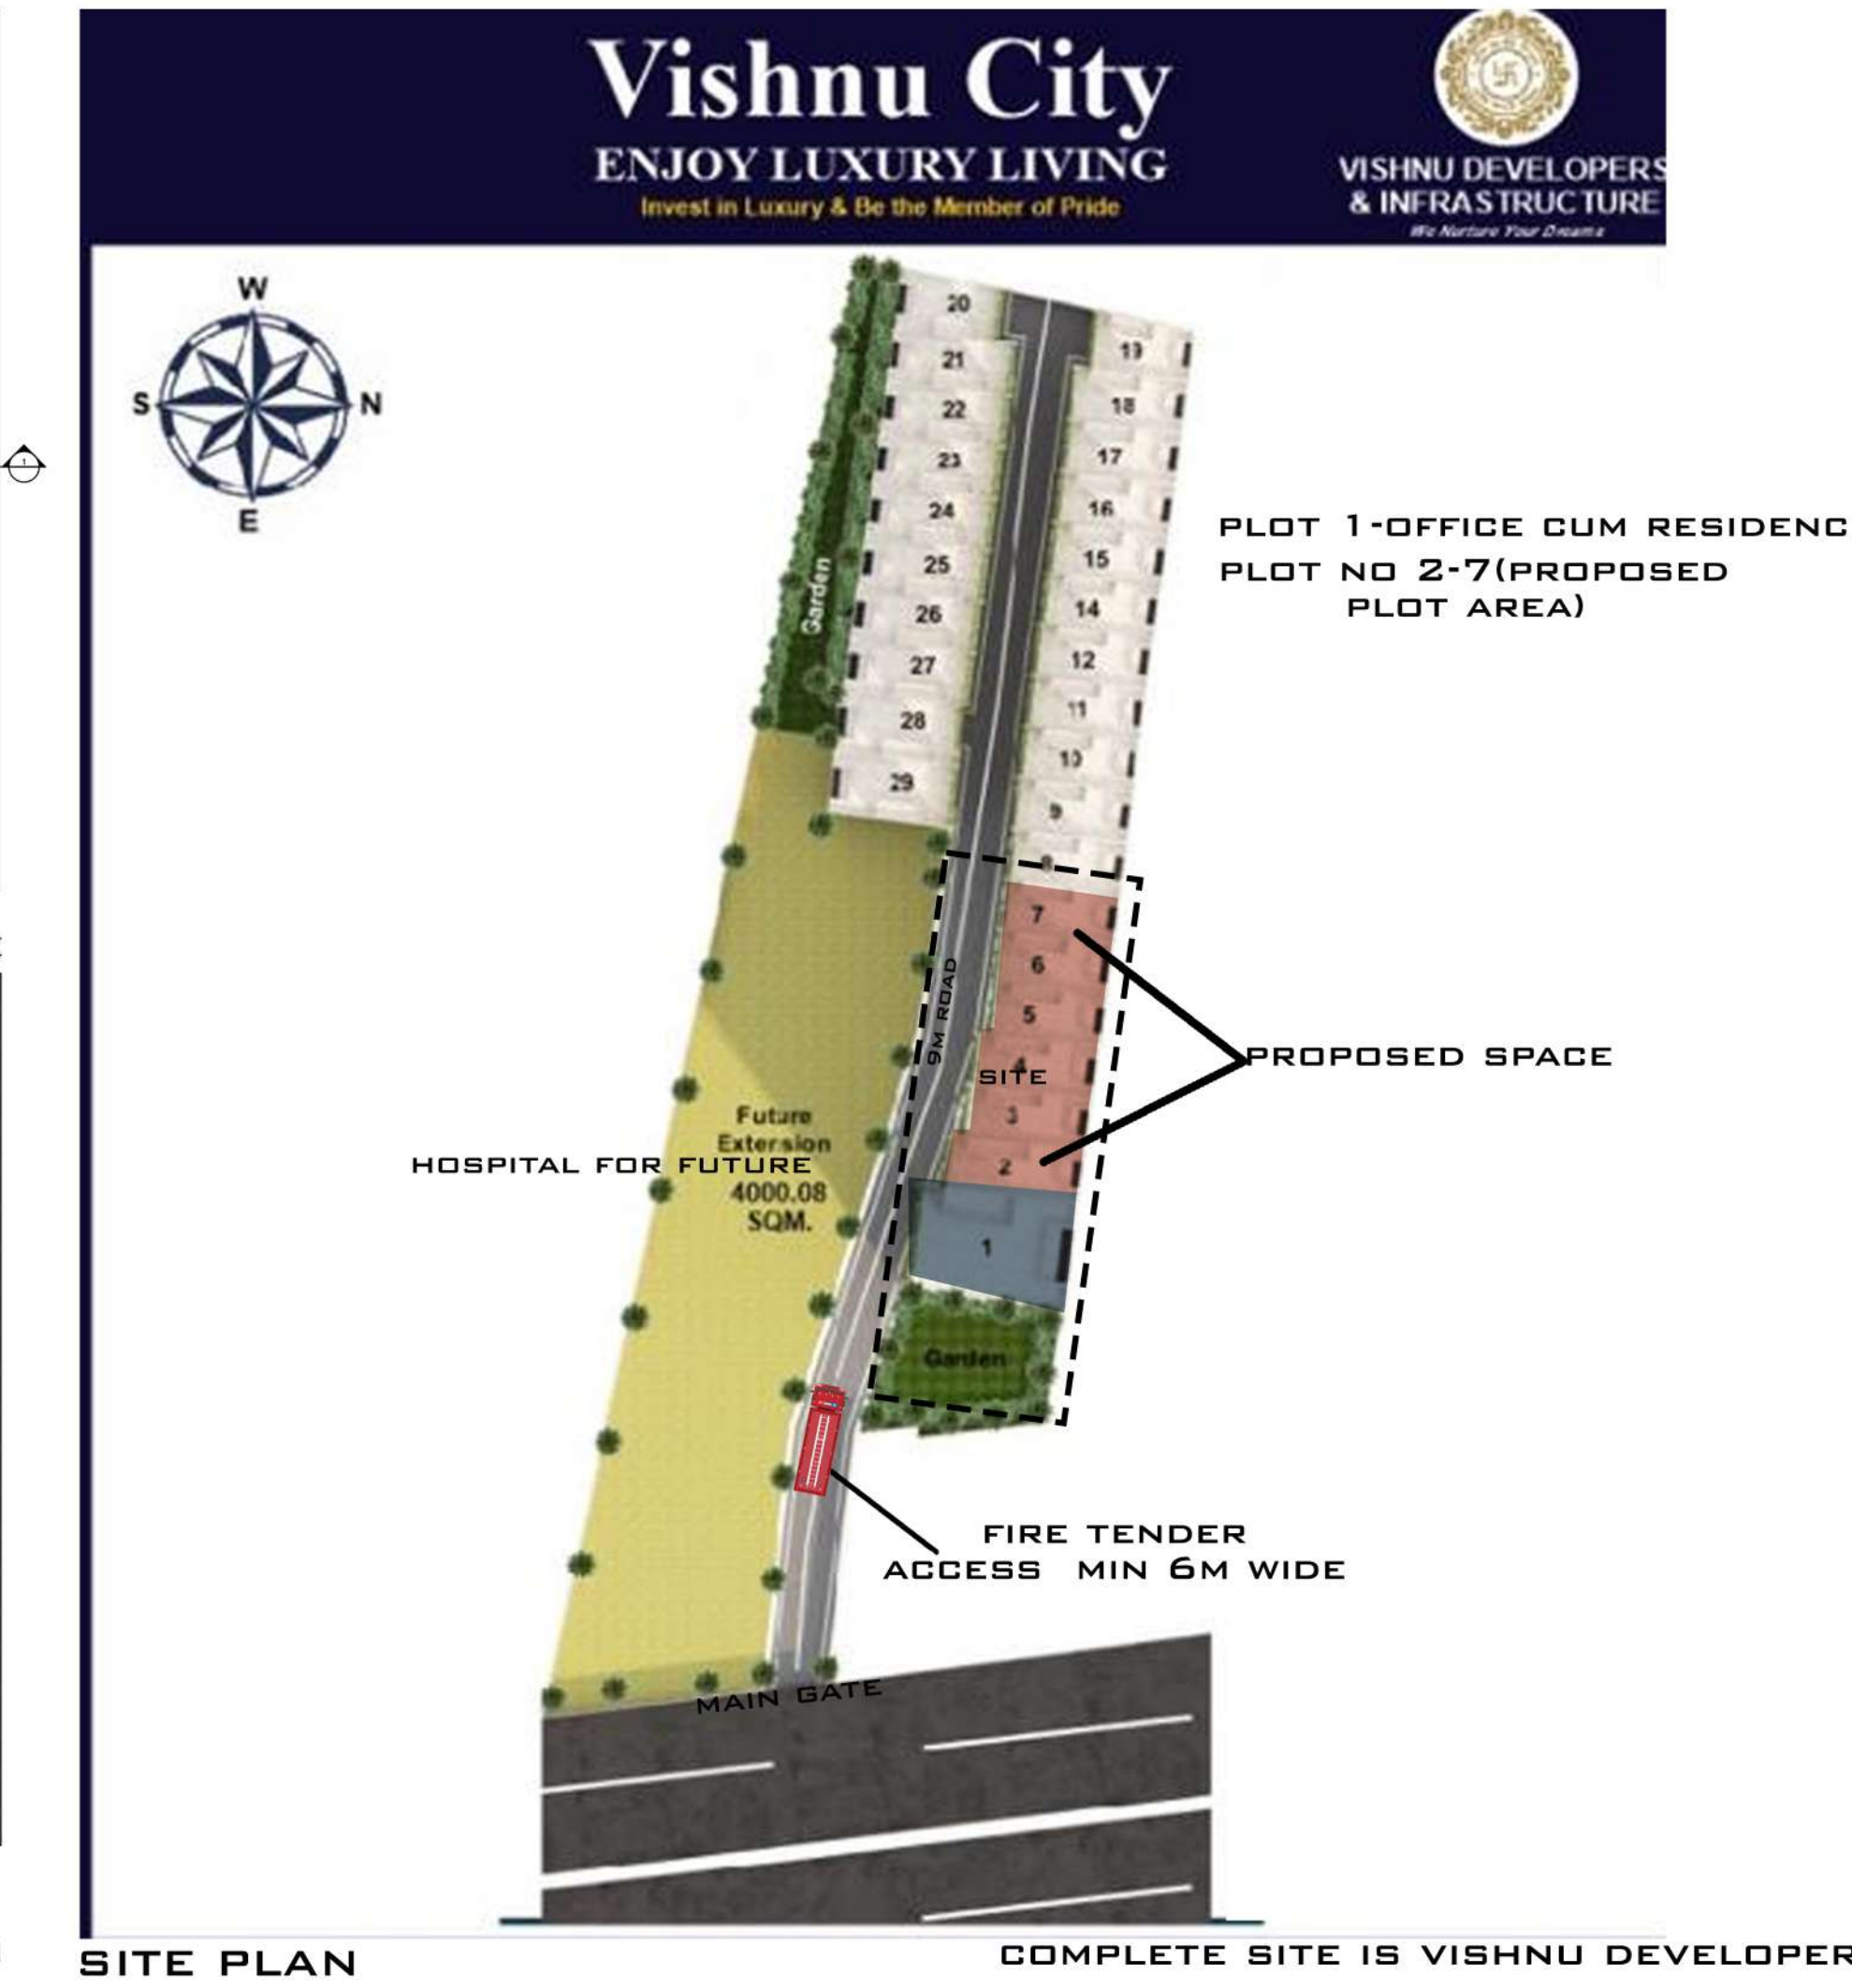
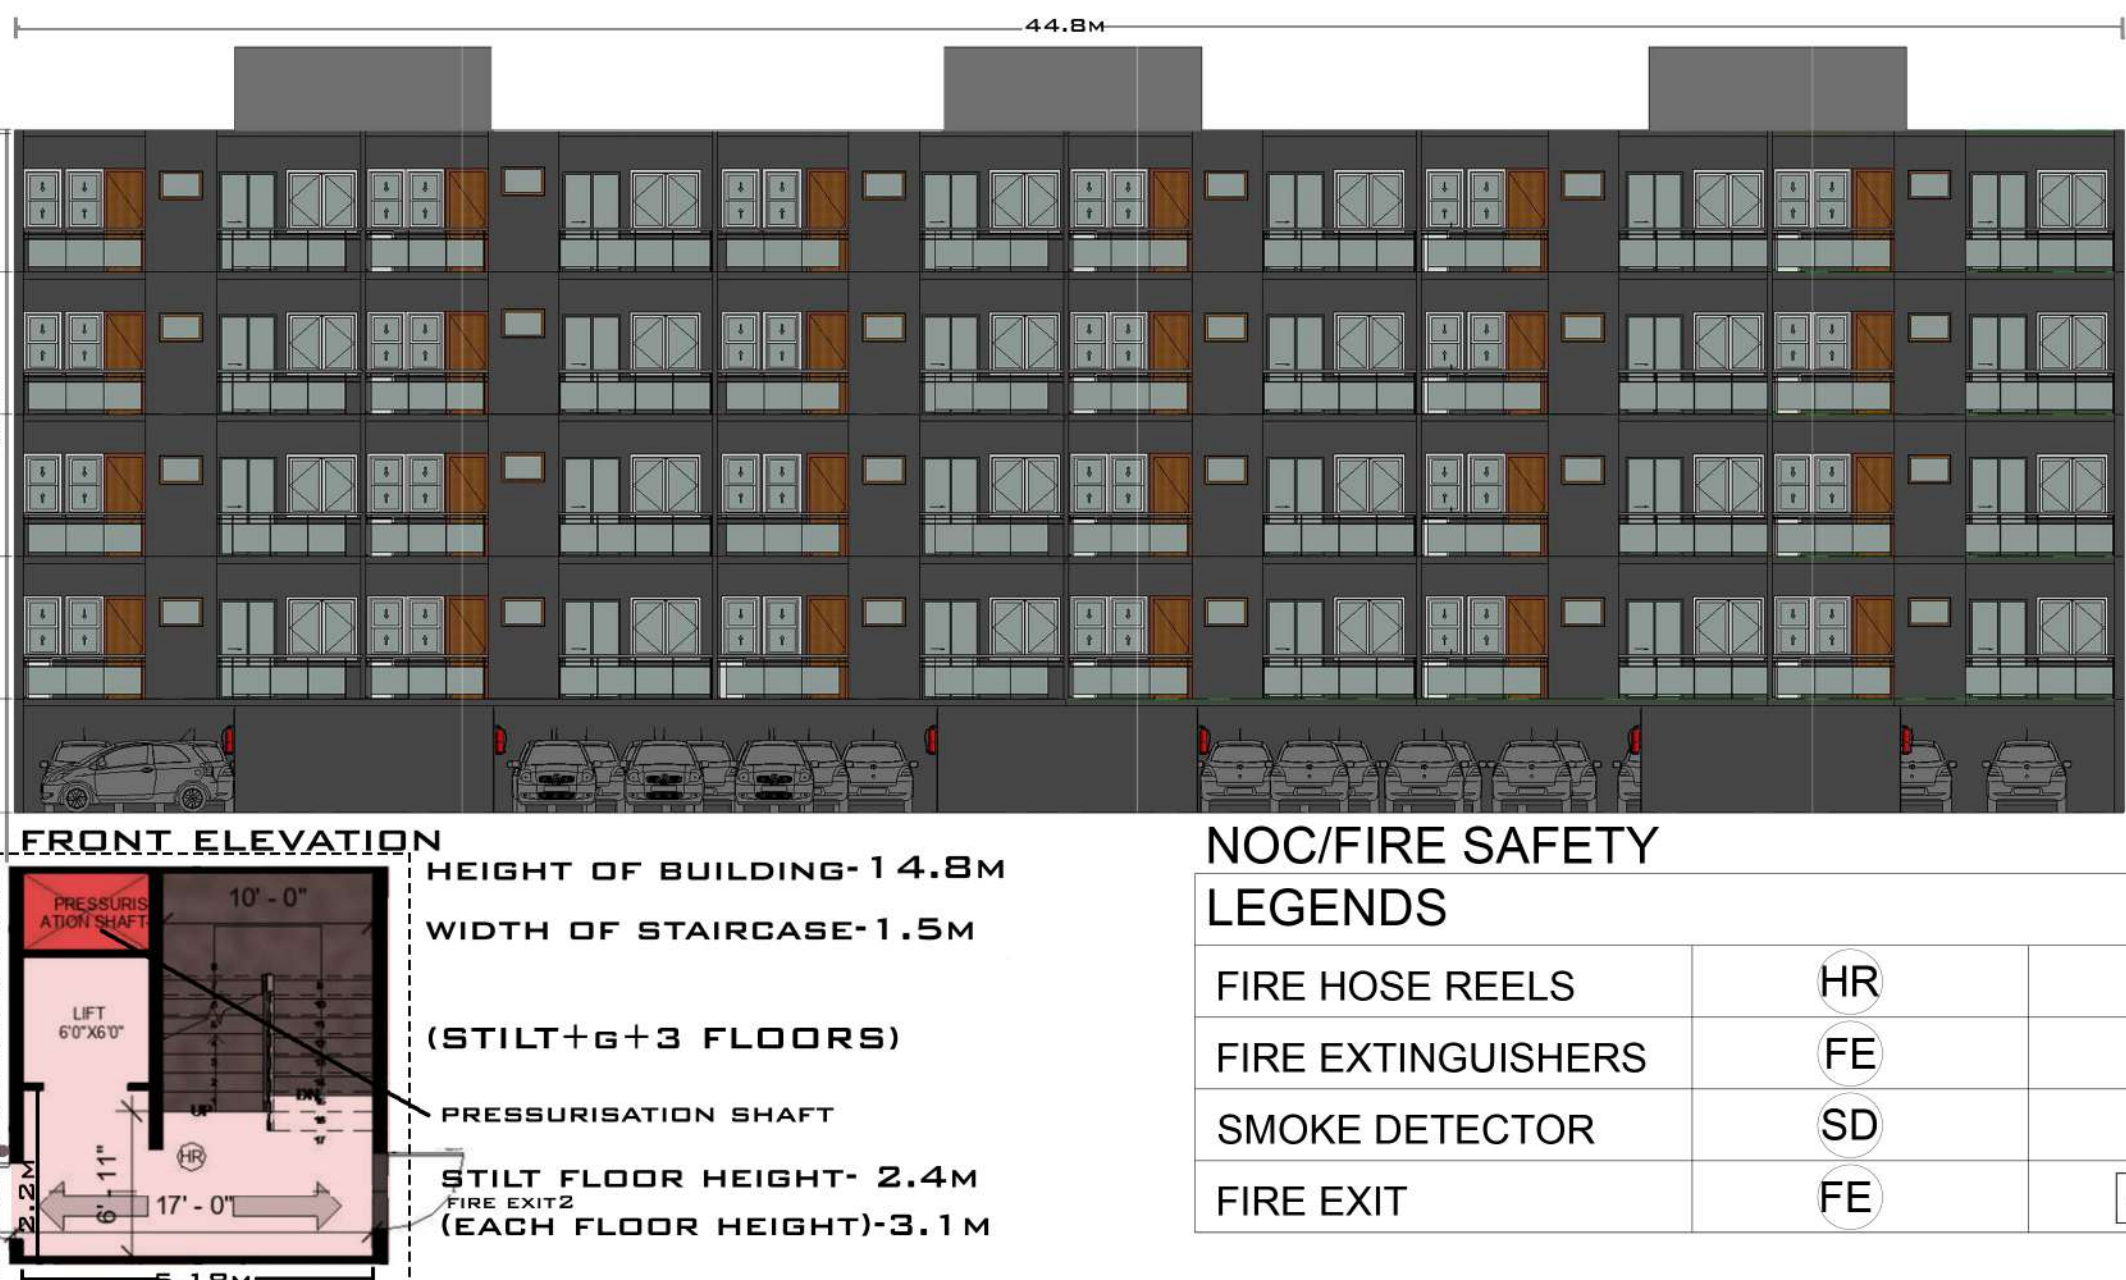
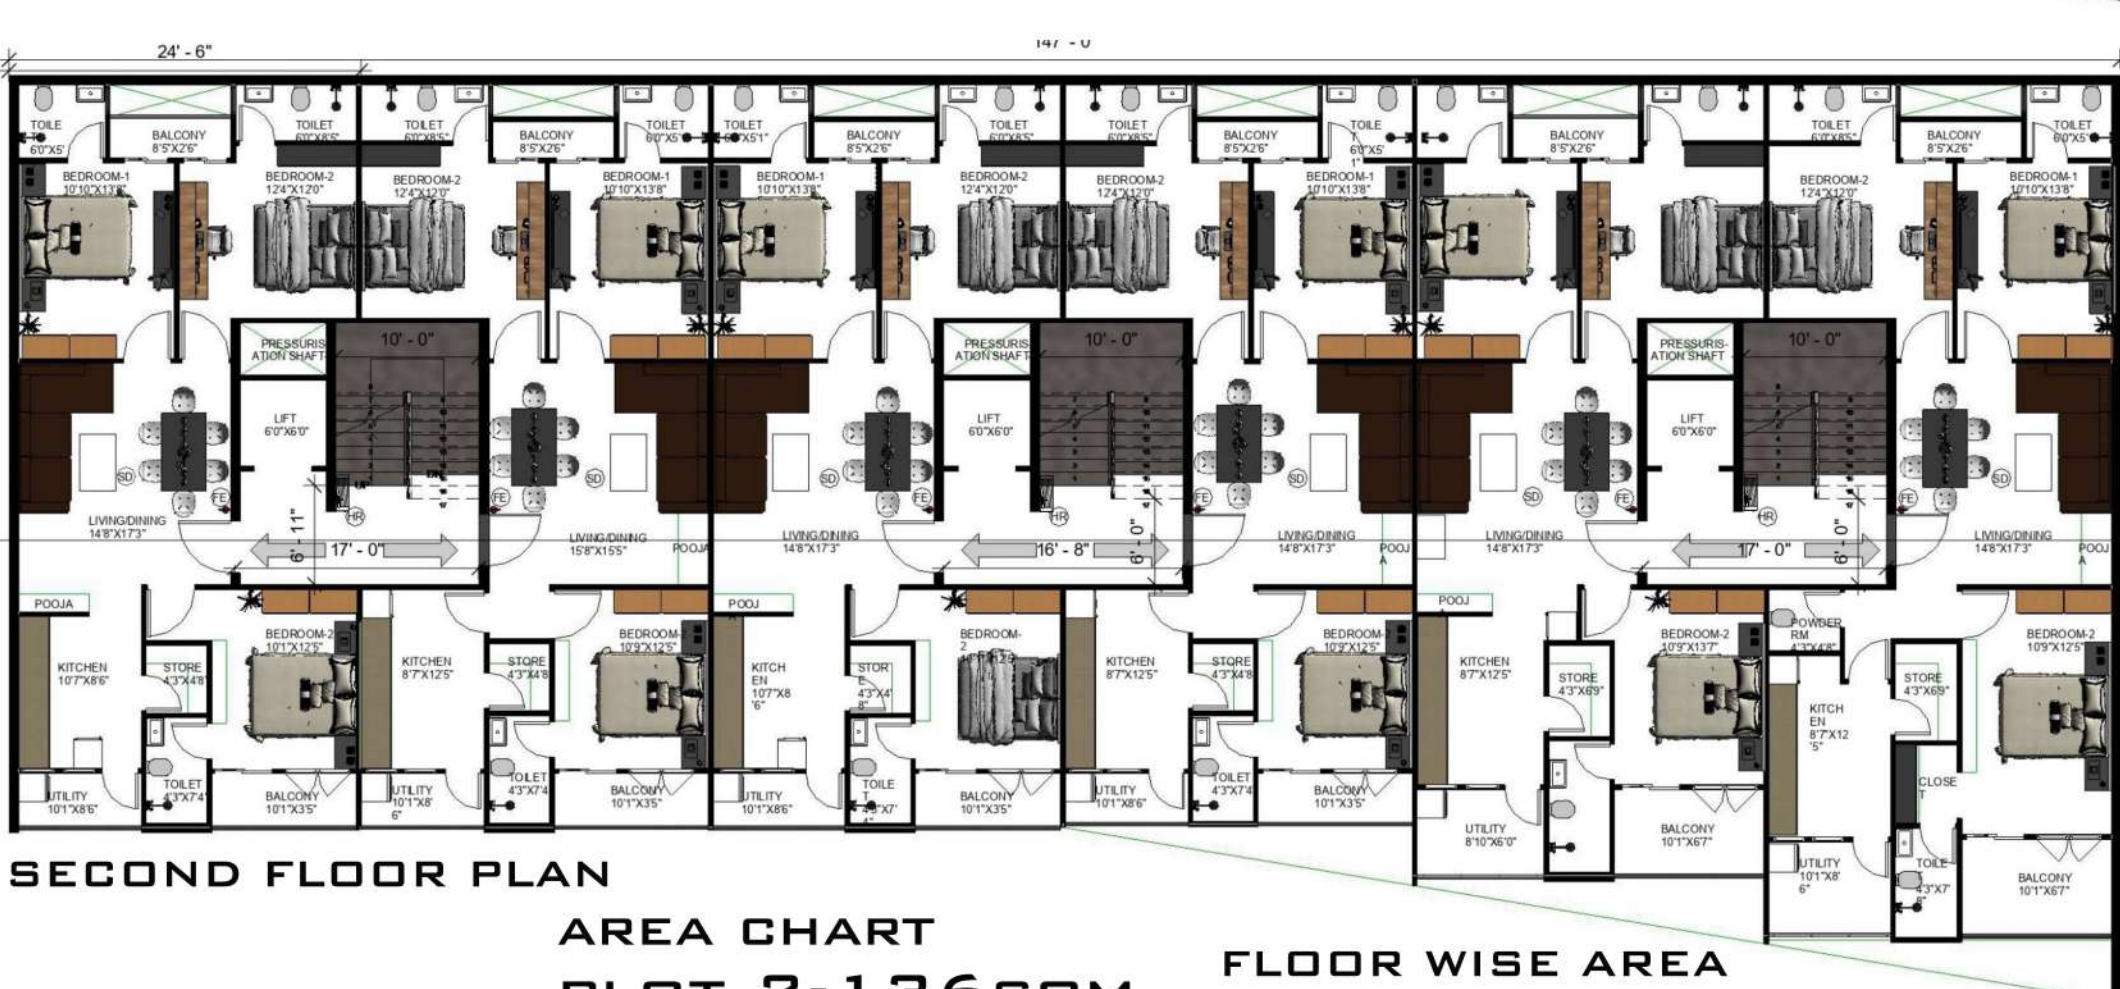
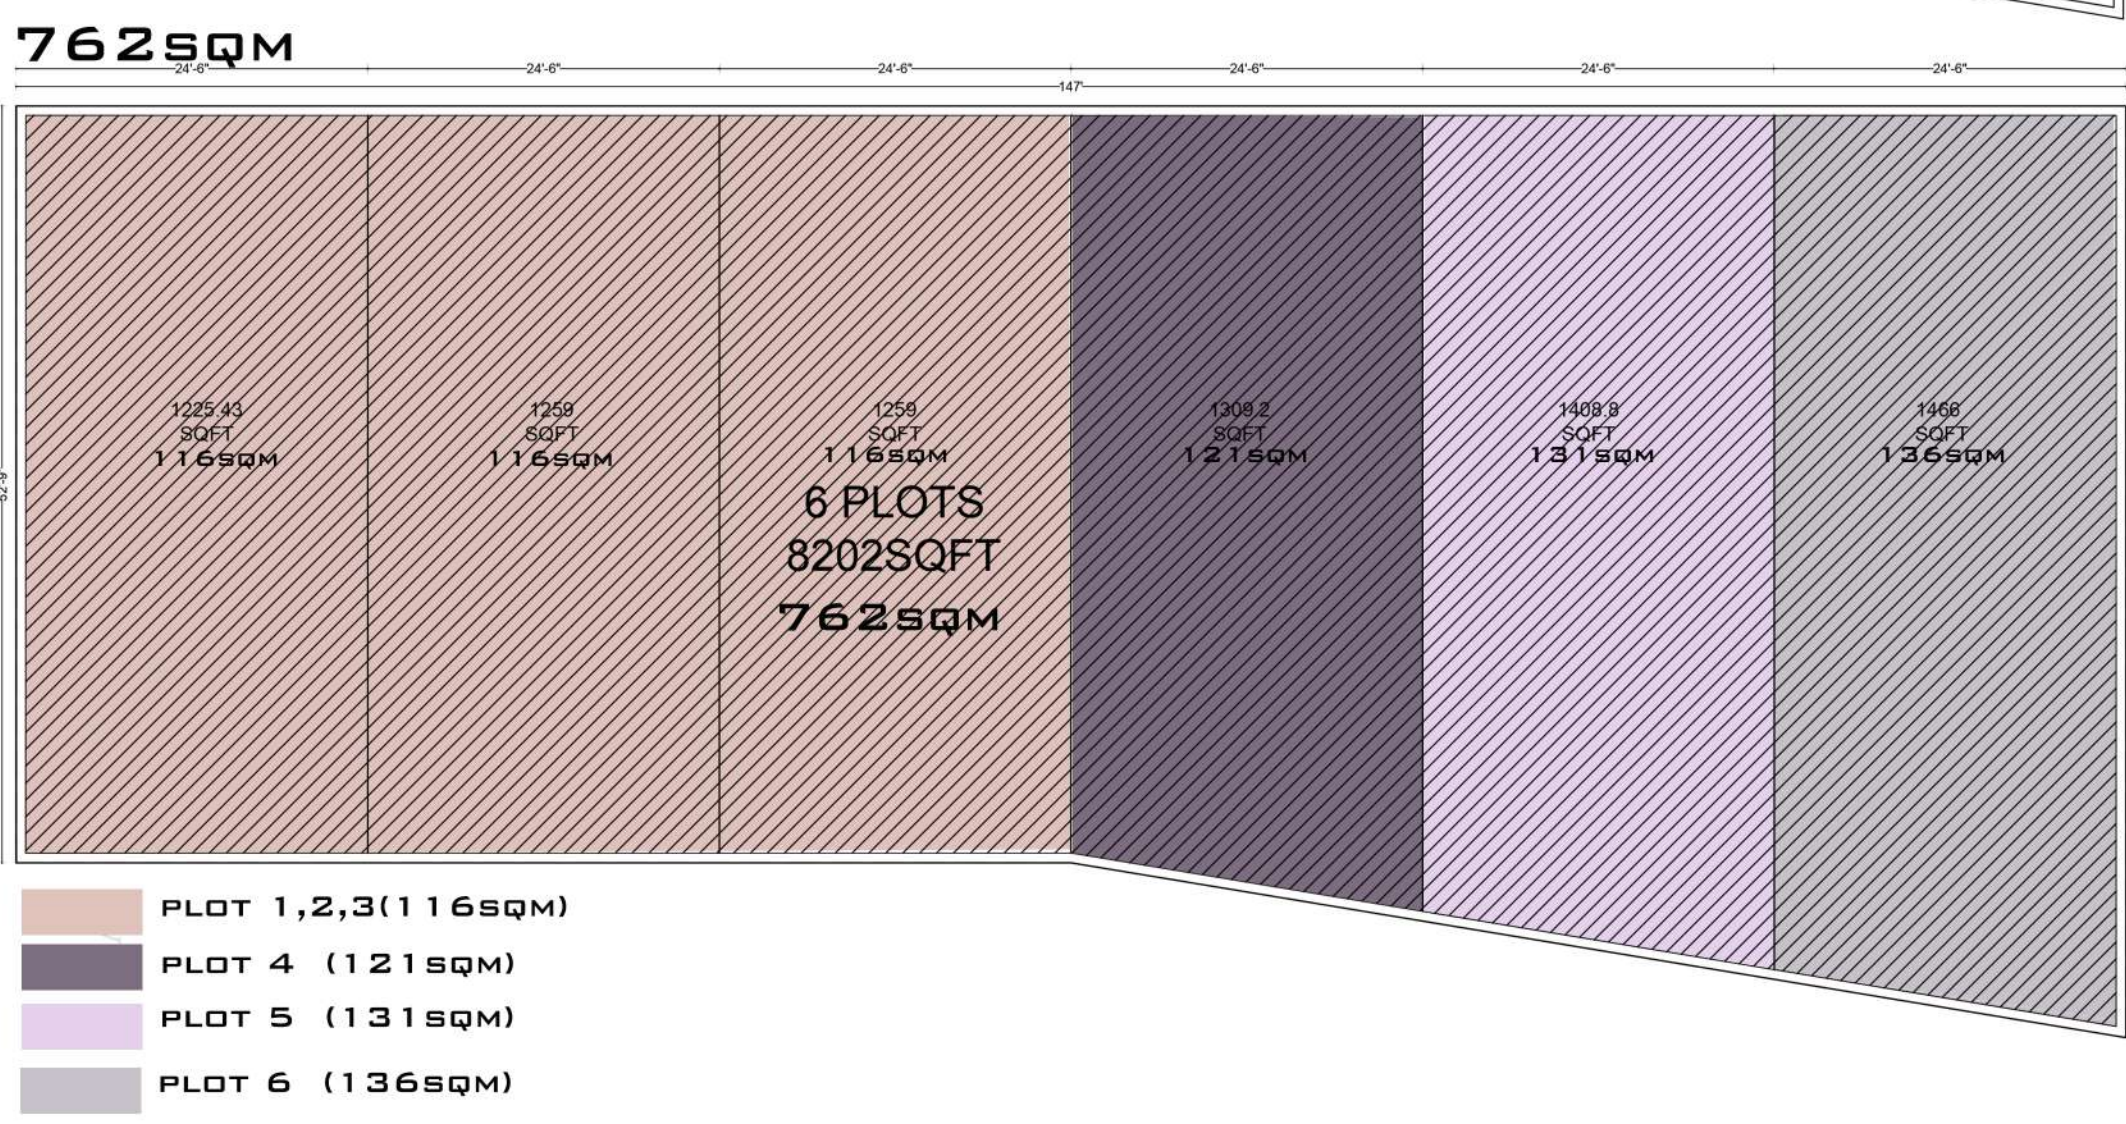
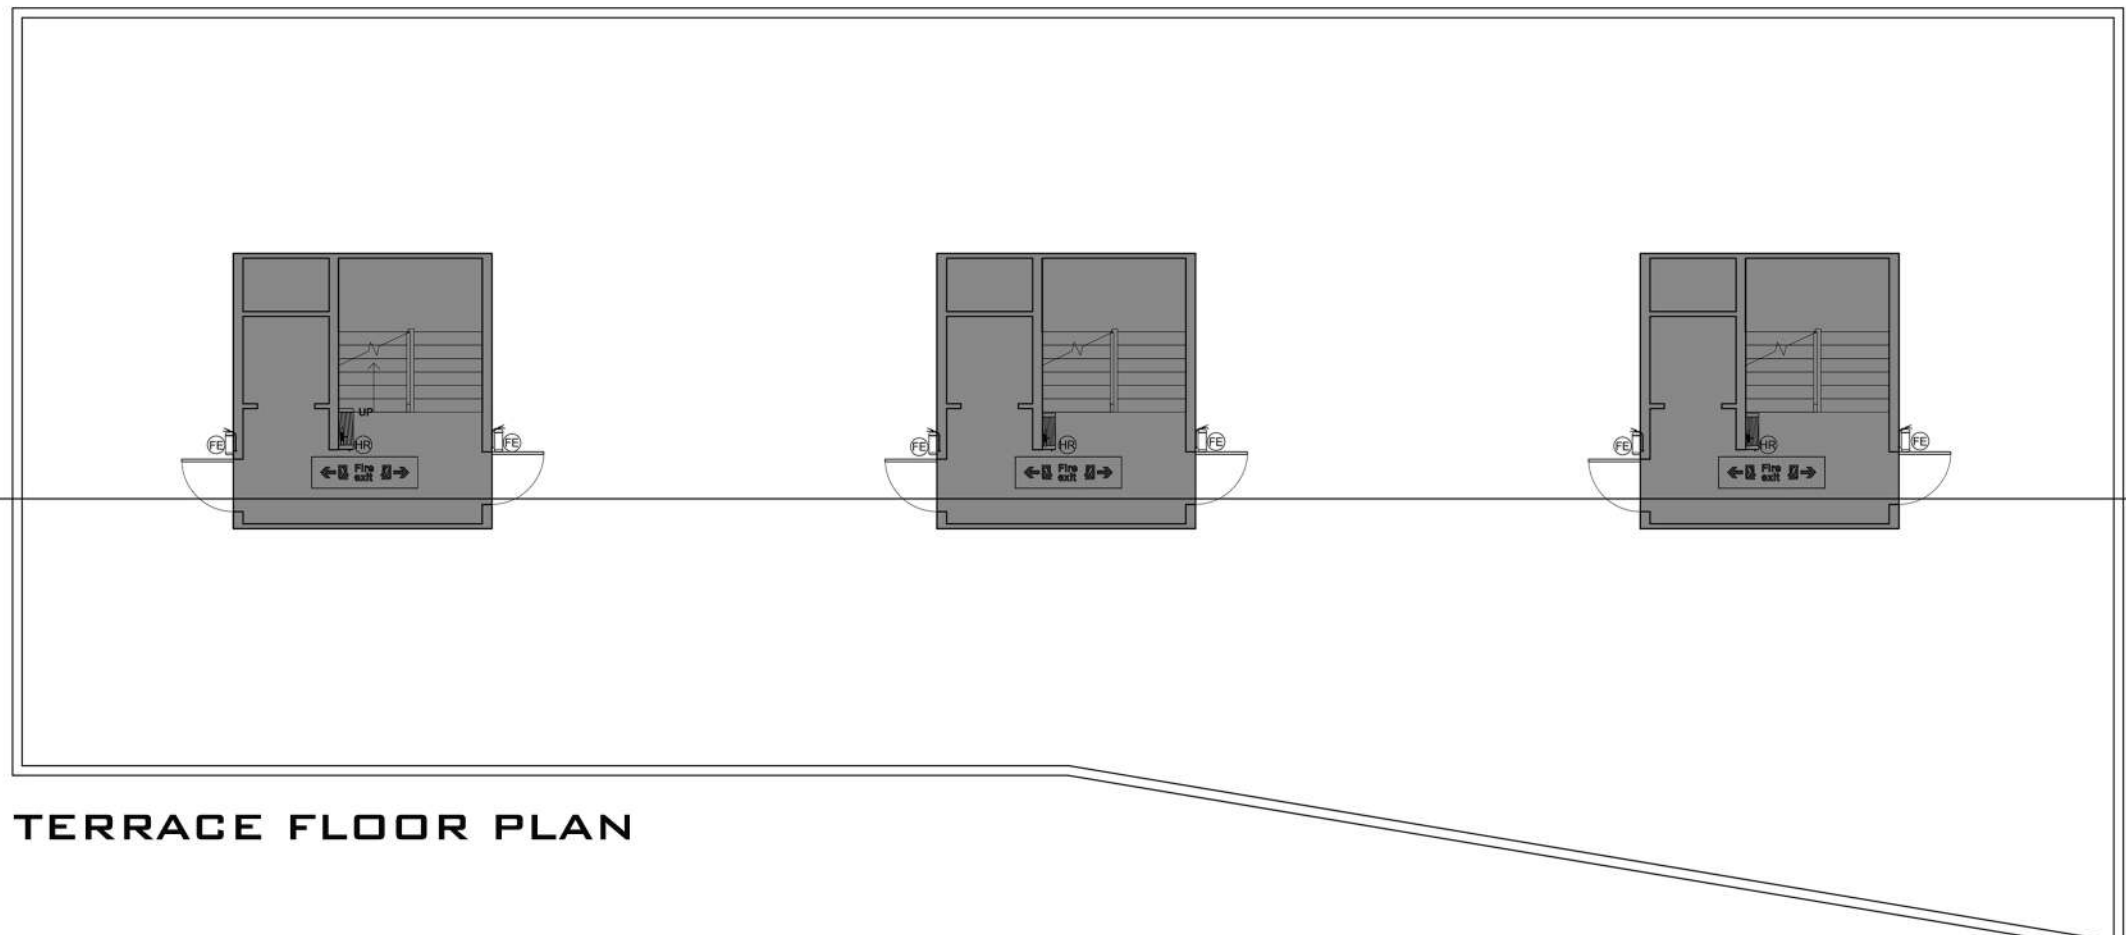
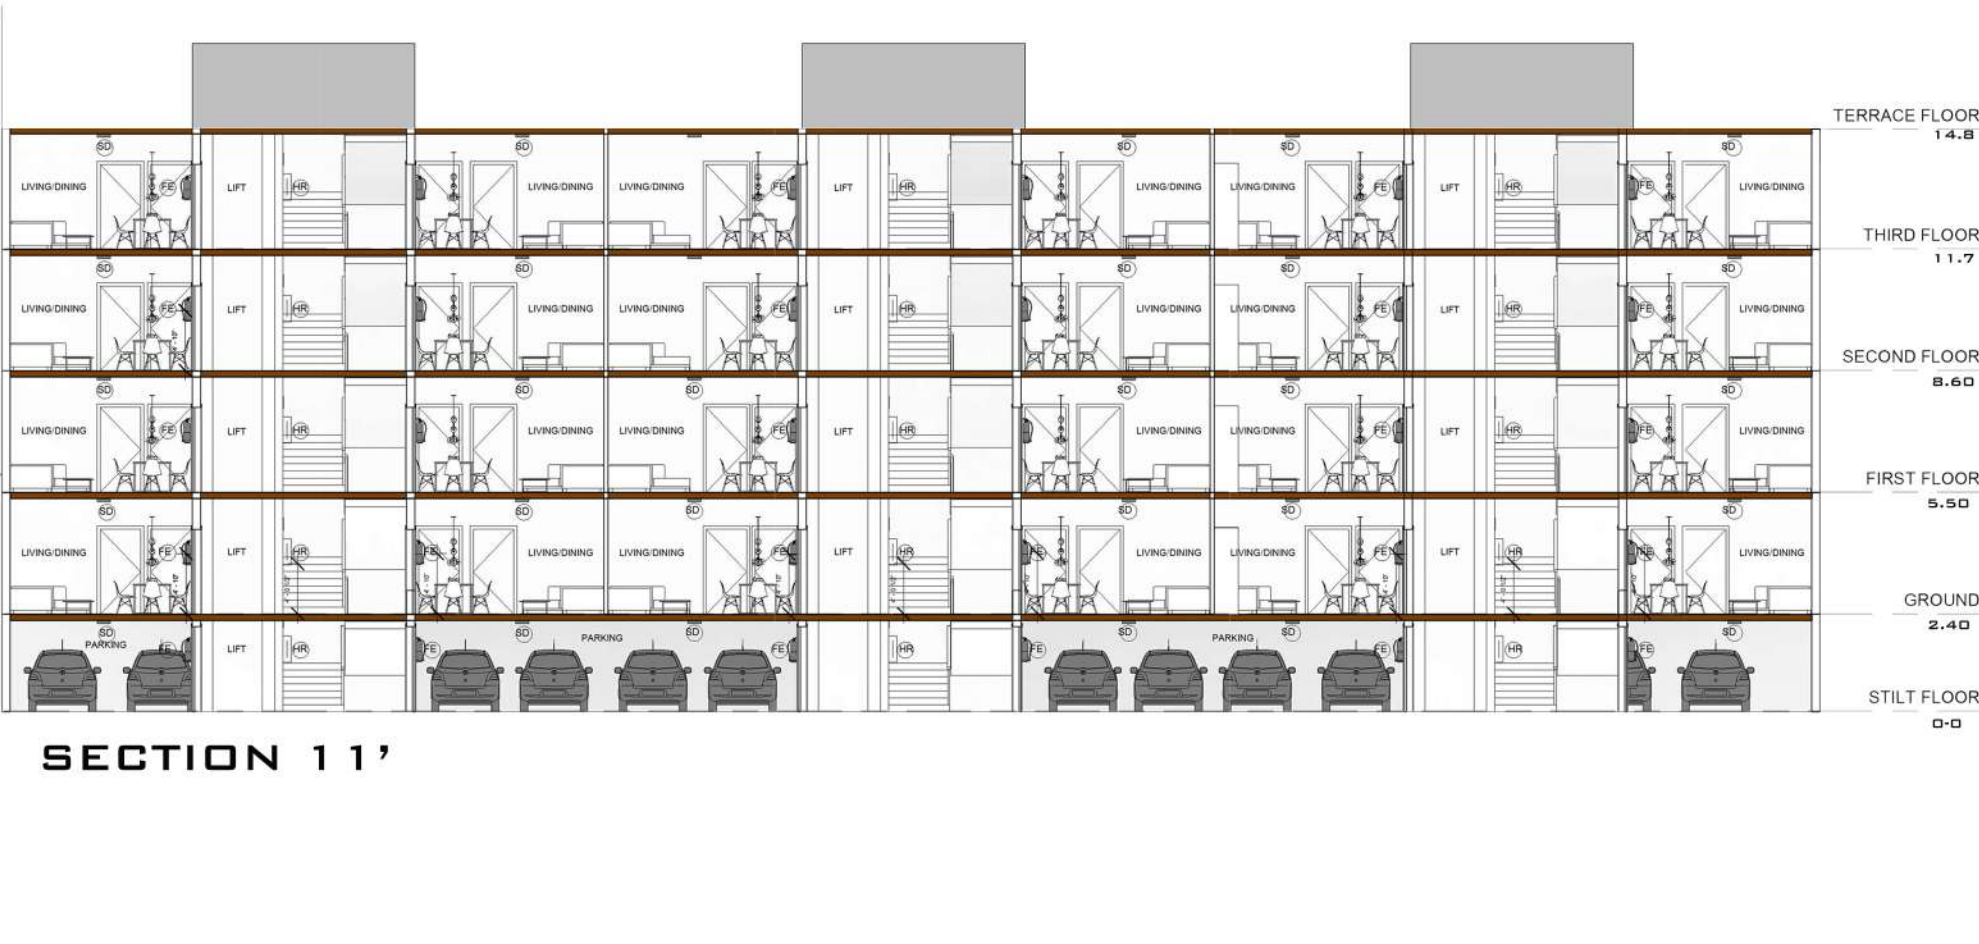


FIRE DRAWING

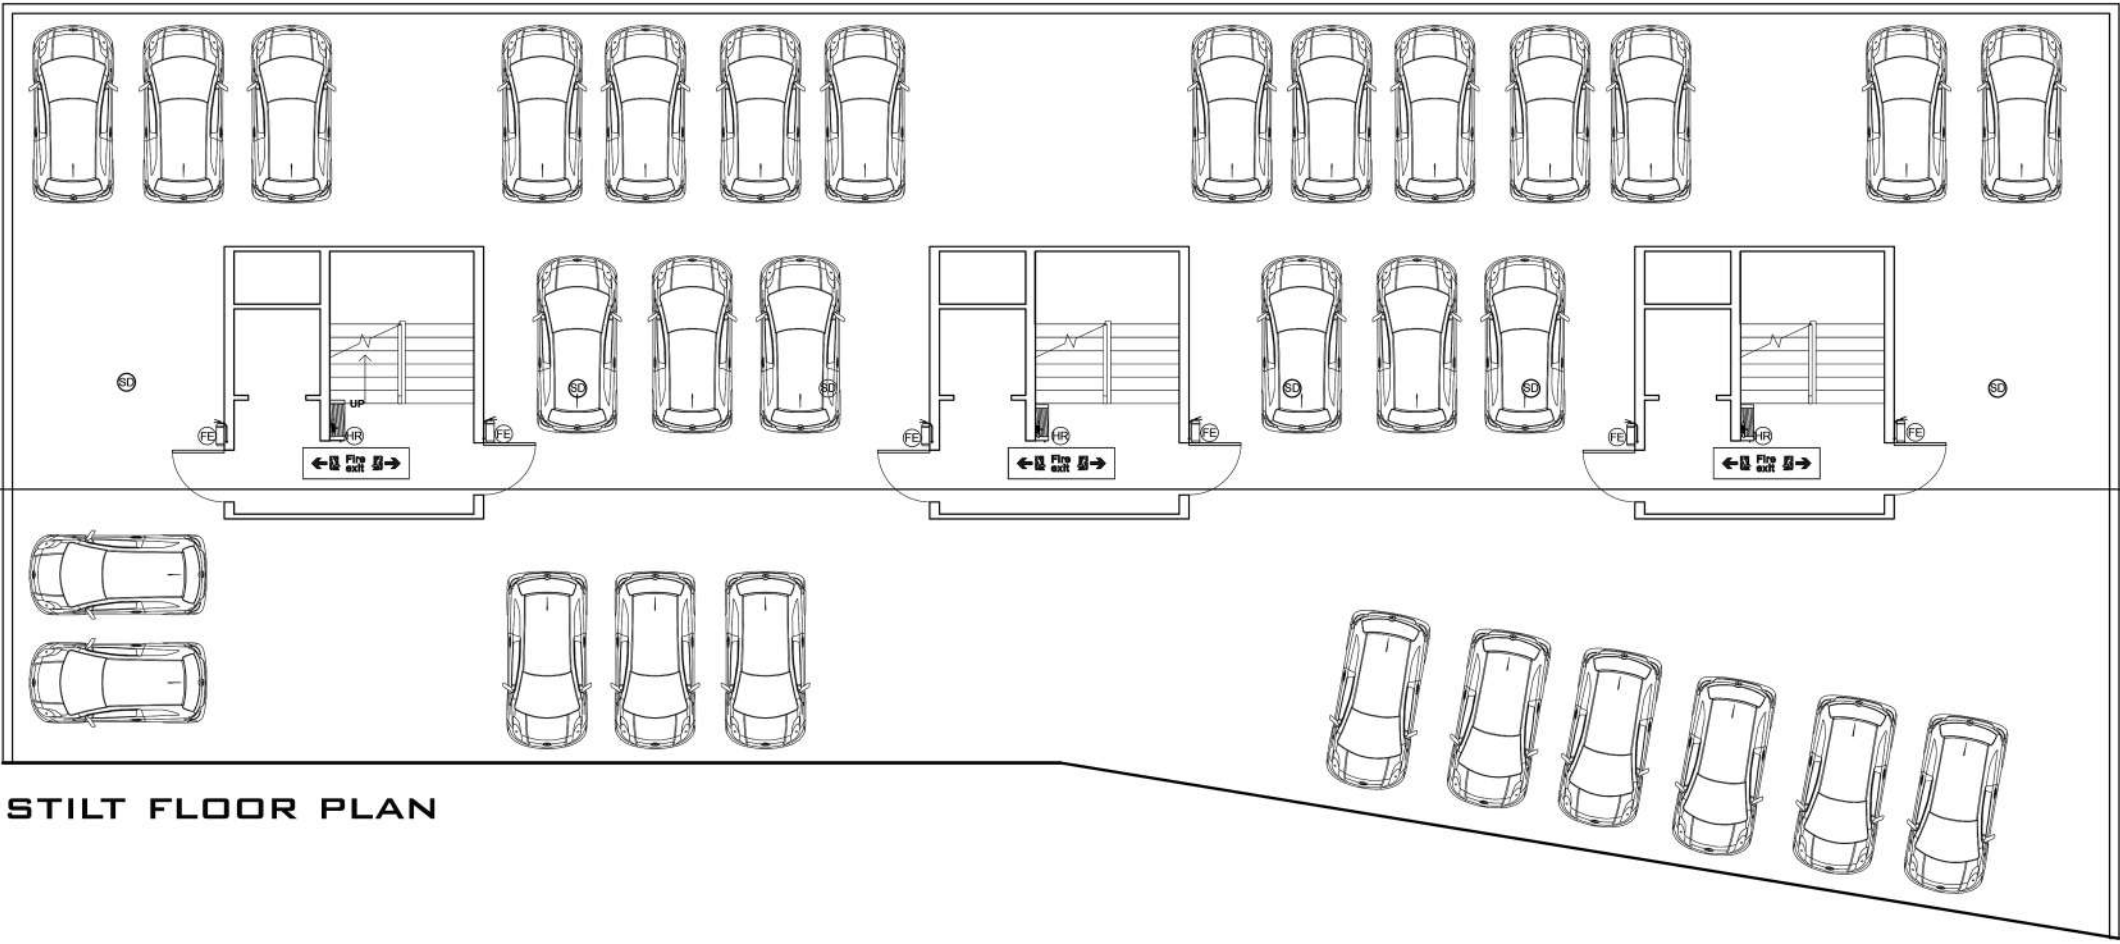

- PROJECT DETAILS
- PLOT AREA-762SQM
 - BUILDING HEIGHT-14.8M
 - STILT+4 FLOORS
 - 3 COMMON STAIRCASE

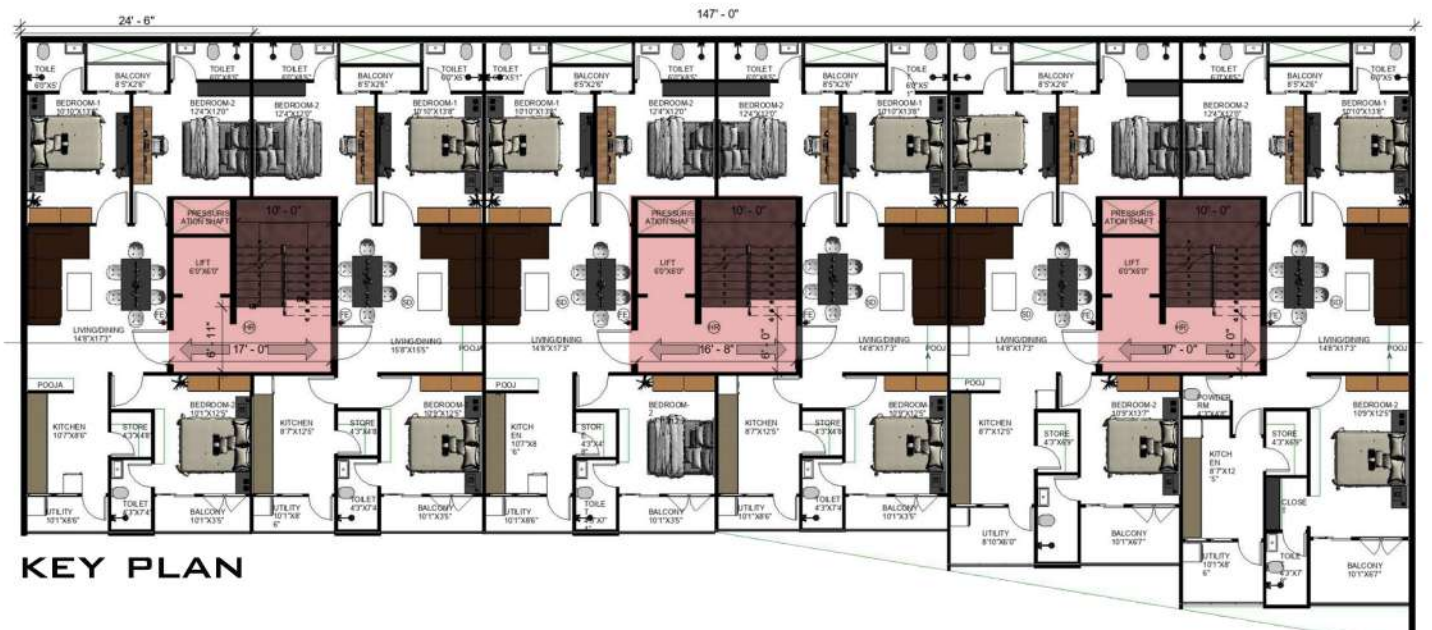

NOC/FIRE SAFETY LEGENDS

FIRE HOSE REELS	HR	
FIRE EXTINGUISHERS	FE	
SMOKE DETECTOR	SD	
FIRE EXIT	FE	